

Project Data

Location	
Parcel Number	
Zoning	RS-50
Lot Size	~101' x ~50' -- ~5000 sq.ft.
Living Area	~1344 sq.ft (BAS), 1-story
Gross Area	1912 sq.ft.
Building Use	Single-Family Residential, Single Unit
Occ. Group	R-3
Const. Type	Type V
Project Scope	Like for like replacement of existing residential windows. No structural modifications, reframing, or changes to existing rough openings. Existing finishes and trim will be repaired or replaced in-kind as needed after removal of old units. No impact to electrical, mechanical, or plumbing systems.
Evacuation Zone	'C'
Flood Zone?	No
Market Value (2025)	\$590,875

General Notes - Window Replacement

- A. Codes, Standards & Product Compliance**

 - Work performed in accordance with:
 - **Florida Building Code 8th Edition (Residential)**
 - **FBC Chapter 3, 6, 7, and 10** (as applicable)
 - **FBC R609 – Windows & Doors**
 - **ASTM E2112 – Standard Practice for Installation of Exterior Windows**
 - **TAS 201/202/203** for impact resistance
 - All installed fenestration complies with **FL14911 (Rev. 12)** Product Approval for the AC 70 Series Single Hung window.
 - HVHZ-rated product accepted for use outside and inside HVHZ zones (City of Tampa).
- B. Existing Conditions / Structural Notes**

 - Existing structure is standard wood-frame residential construction.
 - All existing rough openings verified to meet, at minimum, the listed **"Recommended Rough Opening Width/Height"** from the AC 70 size guide (Page 1).
 - No load-bearing members modified.
 - No sheathing removed.
 - No stucco cut beyond nail-fin perimeter; any exposed areas repaired in-kind.
 - Window replacements do **not** change shear wall capacity, uplift load path, lateral bracing, or diaphragm boundary nailing.
- C. Installation Notes (Anchorage, Fasteners, Shimming)**

 - Nail-fin or through-frame anchorage selected based on existing substrate.
 - Anchorage to follow the Elevation & Anchor Layout Tables (FL14911 Sheet 2).
 - **Anchor spacing:**
 - Jambes: 6" O.C. max (nail fin) or 12.5" O.C. (through-frame)
 - Corners: 3" max from corner (nail fin)
 - **Shimming:**
 - Max shim stack 3/8"
 - Shim each fastener location
 - Maintain uniform frame plumb/square (FL14911 Note #4)
 - **Fasteners:**
 - Wood: #8 or #10 corrosion-resistant screws (per substrate notes)
 - Masonry: 3/16" Tapcon flat-head, 1.25" embedment minimum
 - **Sealants:**
 - Exterior perimeter sealed with compatible elastomeric sealant
 - Backer rod installed where gap exceeds 1/4"

- D. Weatherproofing, Water Management & Flashing**

 - Sill pans installed on all units; pan slope positive to exterior.
 - WRB integrity maintained and integrated with nail-fin flashing.
 - Head flashing overlaps WRB per FBC and ASTM E2112.
 - Jamb flashing shingle-lapped to head flashing.
- E. Energy Performance & Labeling**

 - All windows meet Energy Code requirements for Climate Zone 2.
 - Typical values: U-factor ≤ 0.40, SHGC ≤ 0.25 (varies by glass option; see NFRC labels).
 - NFRC sticker left intact until final inspection.
 - Air infiltration rates per manufacturer certification.
- F. Safety Glazing Requirements / Hazardous Locations**

 - Per **FBC R308**, laminated impact glazing inherently complies with safety-glazing requirements.
 - Hazardous locations include:
 - Within 24" arc of doors
 - Above tubs/showers
 - Near stair landings
 - Adjacent to walking surfaces
 - AC 70 laminated units meet safety glazing standards and do not require tempered glass.
- G. Demolition & Disposal Notes**

 - Existing windows removed with minimal disturbance to stucco/trim.
 - Exposed areas patched with like materials (stucco, cement board, or siding).
 - All debris removed from site daily.
- H. Homeowner/Builder + Licensed Installer Notes**

 - Permit obtained under **Homeowner-Builder Exemption** (Florida Statutes §489.103(7)).
 - A **licensed contractor** experienced with AC 70 Series installation will perform or supervise all work.
 - Licensed contractor will be onsite for all installation activities covered under FBC.


- I. Inspection Notes**

 - Rough opening inspection: **N/A** (existing openings; no structural work).
 - Window installation inspection: Verify anchorage, sealants, shims, flashing.
 - Final inspection: Verify NFRC stickers present, HVHZ glazing, proper function of single-hung units, and weather sealing.
 - Egress windows: Verified equal or greater than existing opening area.



Points of Contact

Contractor:

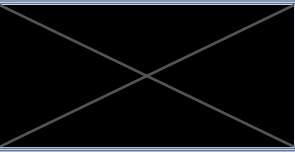

Project Manager/Author:

Justin Lenhart



Author's Note

These drawings were prepared by the homeowner's authorized agent for the purpose of permitting a like-for-like residential window replacement. I am not a licensed architect, engineer, or design professional. The plans are based on field measurements, manufacturer data, and publicly available building code requirements. While not a sealed design prepared by a licensed design professional, the information presented is accurate to the best of my knowledge and intended to provide clear documentation of the scope of work.


The scope of this project is limited to replacement of existing windows with new impact-rated units of equivalent size. No structural modifications to existing rough openings are proposed. All replacement products have current Florida Product Approval (FL14911) and comply with applicable requirements for the City of Tampa and the Florida Building Code.

Installation will be performed by a licensed window contractor, and all work will comply with manufacturer instructions, applicable code sections, and standard trade practice. Any code-required inspections will be scheduled and coordinated through the City of Tampa's permitting system.

These drawings are provided in good faith to assist reviewers and inspectors by clearly documenting existing conditions, product selections, and installation intent. If any discrepancies arise, the requirements of the Florida Building Code and manufacturer installation instructions will govern.

Justin Lenhart

Address:

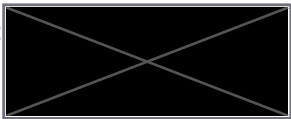

Made by : Justin Lenhart

Date : 24 Nov 2025




Tampa, FL

A0.1

Notes and References


SCALE:
N/A

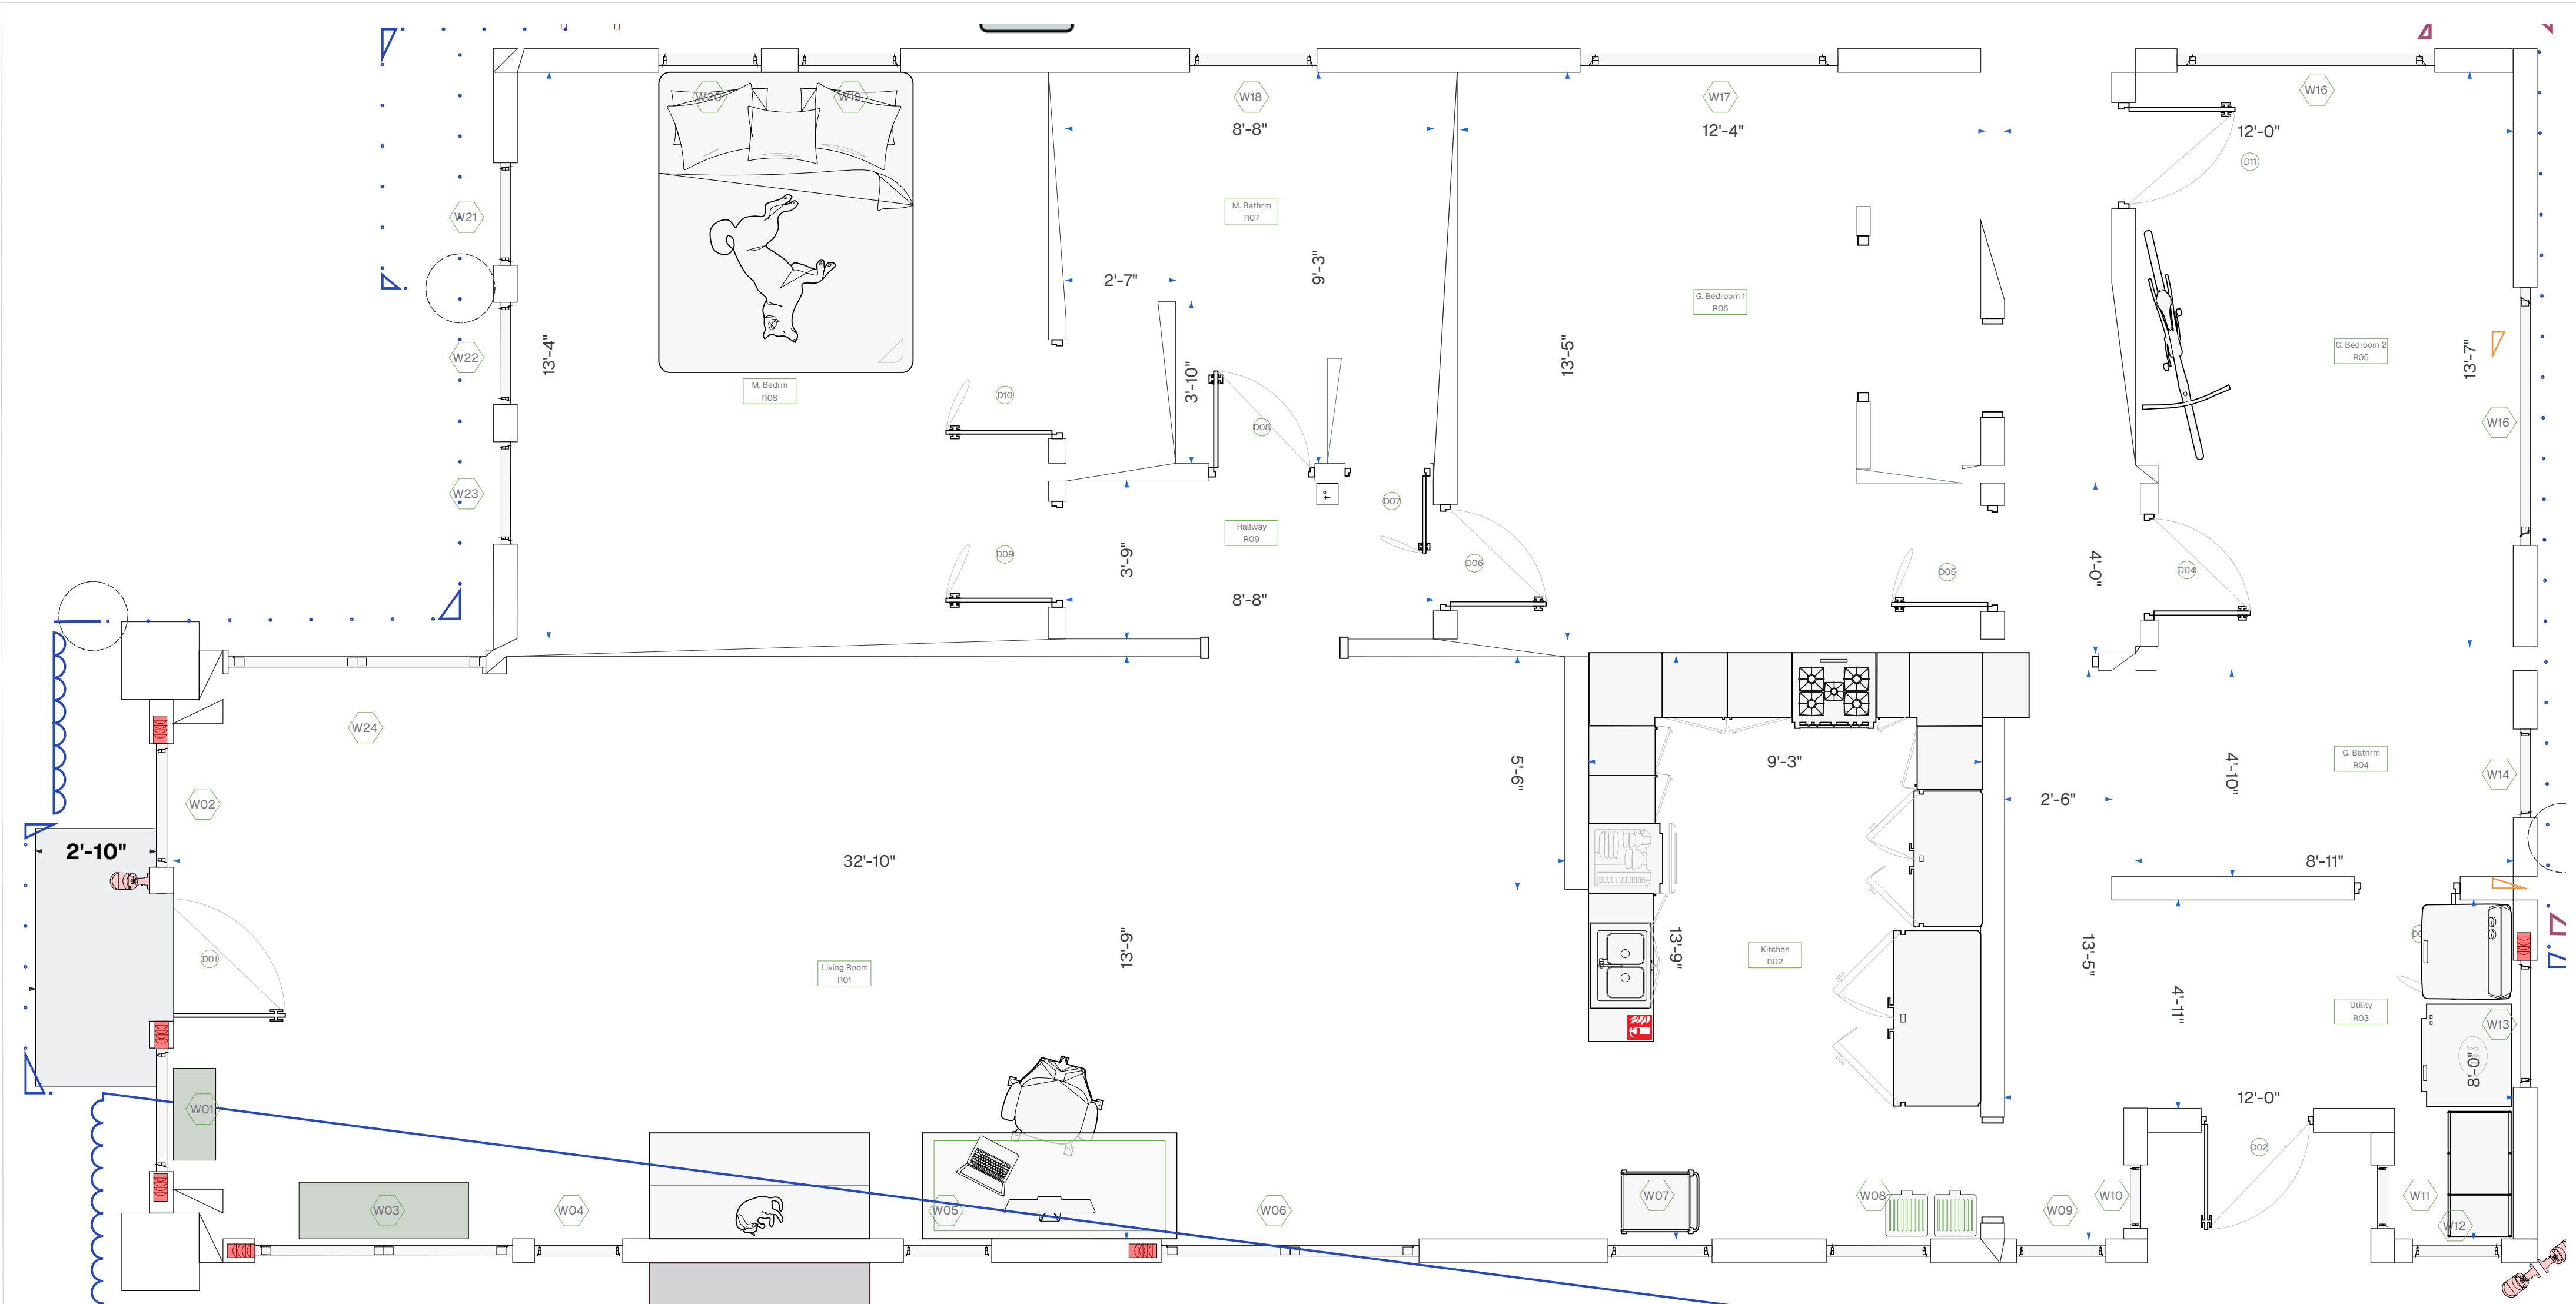

Tag ID	Window Size	Rough Width	Rough Height	Current Window Type	Tag ID	Window Size	Rough Width	Rough Height	Current Window Type		
 W01	W01	2450	35"	61"	Single Hung	 W13	W13	3030	36"	36"	Single Hung
 W02	W02	2450	35"	61"	Single Hung	 W14	W14	2030	25-1/4"	36"	Single Hung
 W03	W03	3050-2	73"	61"	Double Single Hung	 W15	W15	3040-2	72"	49"	Double Single Hung
 W04	W04	2038	25"	45"	Single Hung	 W16	W16	3040-2	72"	49"	Double Single Hung
 W05	W05	2038	24-1/2"	42-1/2"	Single Hung	 W17	W17	3040-2	72"	49"	Double Single Hung
 W06	W06	3050-2	73"	61"	Double Single Hung	 W18	W18	3032	37"	38"	Single Hung
 W07	W07	2430	29-1/2"	36-1/2"	Jalousie	 W19	W19	2450	29"	50-3/4"	Jalousie
 W08	W08	2430	29-1/2"	36-1/2"	Jalousie	 W20	W20	2450	29"	50-3/4"	Jalousie
 W09	W09	2030	25-1/4"	37"	Jalousie	 W21	W21	2450	29"	50-3/4"	Jalousie
 W10	W10	1630	18"	37"	Jalousie	 W22	W22	2450	29"	50-3/4"	Jalousie
 W11	W11	1630	18"	37"	Jalousie	 W23	W23	2450	29"	50-3/4"	Jalousie
 W12	W12	2030	25-1/4"	37"	Jalousie	 W24	W24	3050-2	73"	61"	Double Single Hung

Tag name	Name	Rough Width	Rough Height	Swing Direction	Swing Type
D01	Front Door	30"	80"	Right	In
D02	Back Door	31-3/4"	80"	Right	Out
D03	Guest Bathroom Door	18-1/2"	80"	Left	Out
D04	Guest Bedroom 2 Door	30"	80"	Right	In
D05	Guest Bedroom 1 Door 2	30"	80"	Left	In
D06	Guest Bedrm 1 Door 1	30"	80"	Right	In
D07	Hallway Closet Door	24"	80"	Left	Out
D08	Master Bathroom Door	30"	80"	Left	In
D09	Master Bedroom Door	30"	80"	Left	In
D10	Master Bedrm Closet Door	28"	80"	Left	Out
D11	G_Bedrm2ClDoor	30"	80"	Left	Out
D12	ShedDoor	32"	80"	Right	Out

	Name	Room Name	Area
Living Room R01	R01	Living Room	450 sq.ft.
Kitchen R02	R02	Kitchen	133 sq.ft.
Utility R03	R03	Utility	109 sq.ft.
G. Bathrm R04	R04	Guest Bathroom	45 sq.ft.
G. Bedrm 2 R05	R05	Guest Bedroom 2	136 sq.ft.
G. Bedrm 1 R06	R06	Guest Bedroom 2	178 sq.ft.
M. Bathrm R07	R07	Master Bathroom	65 sq.ft.
M. Bedrm R08	R08	Master Bedroom	180 sq.ft.
Hallway R09	R09	Hallway	40 sq.ft.

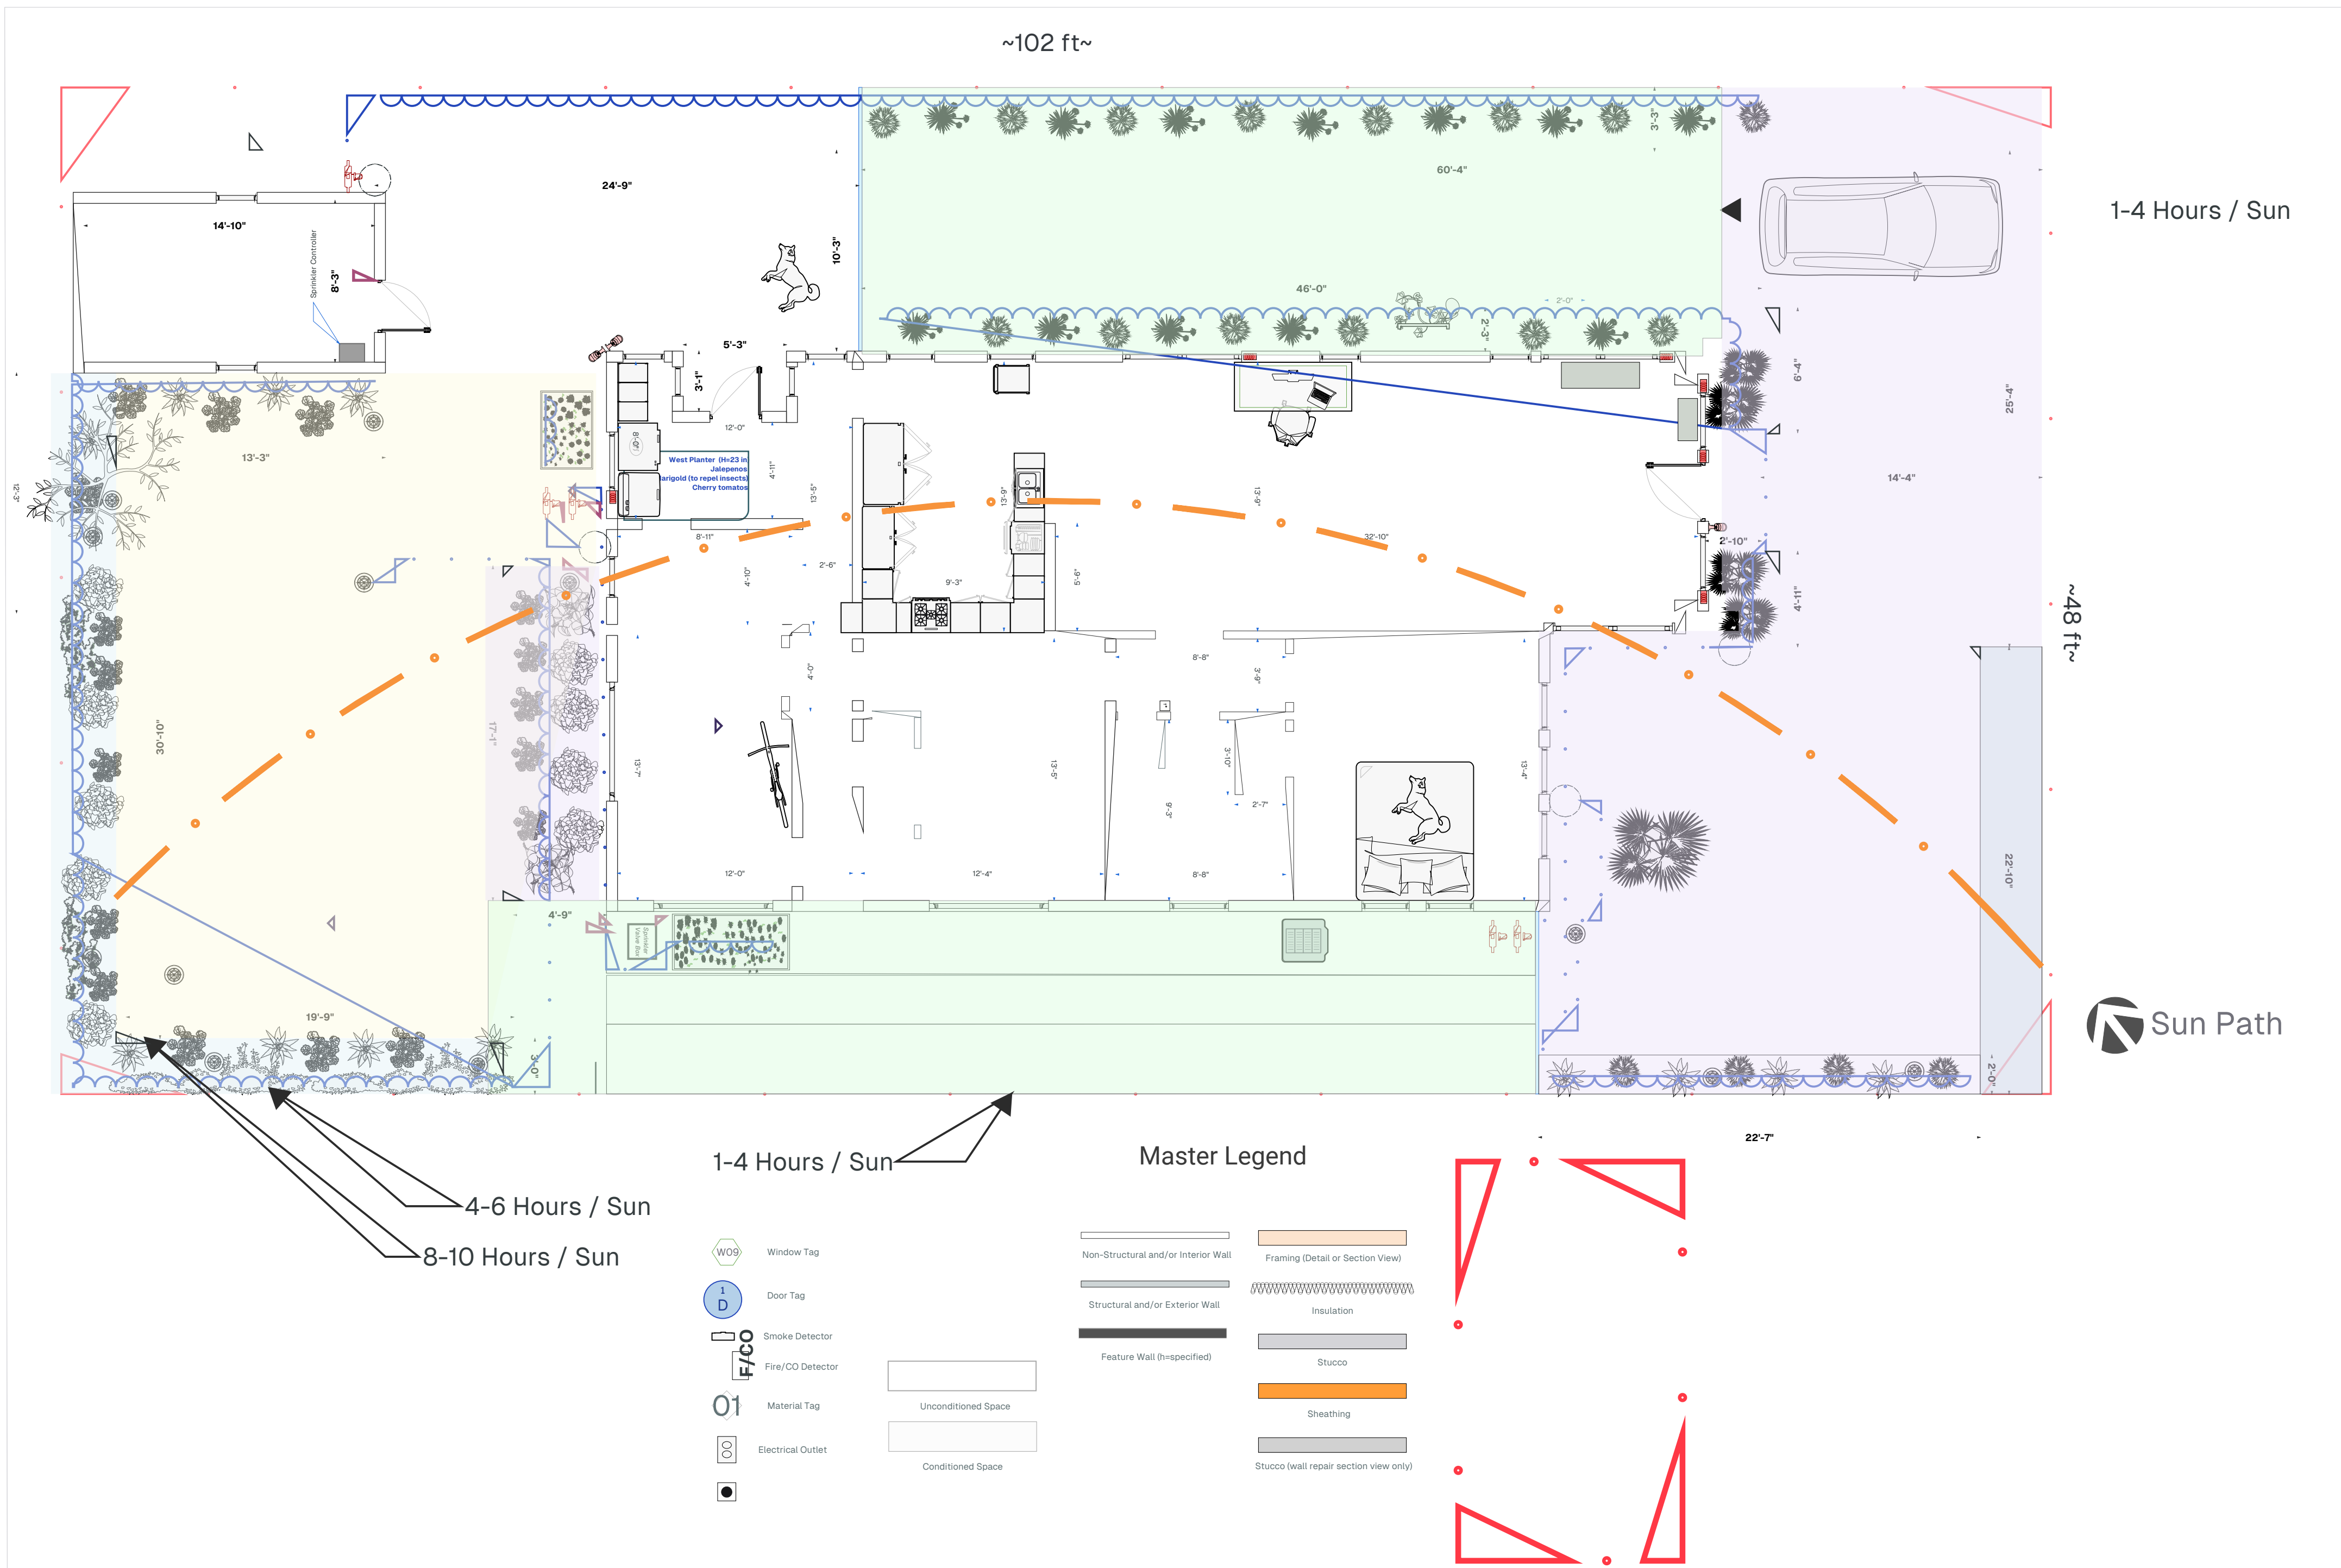

1.3


Sun Diagram


SCALE
1:3/16

Address:

Made by : Justin Lenhart

Date : 24 Nov 2025

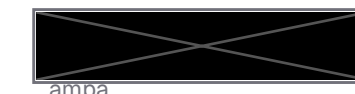


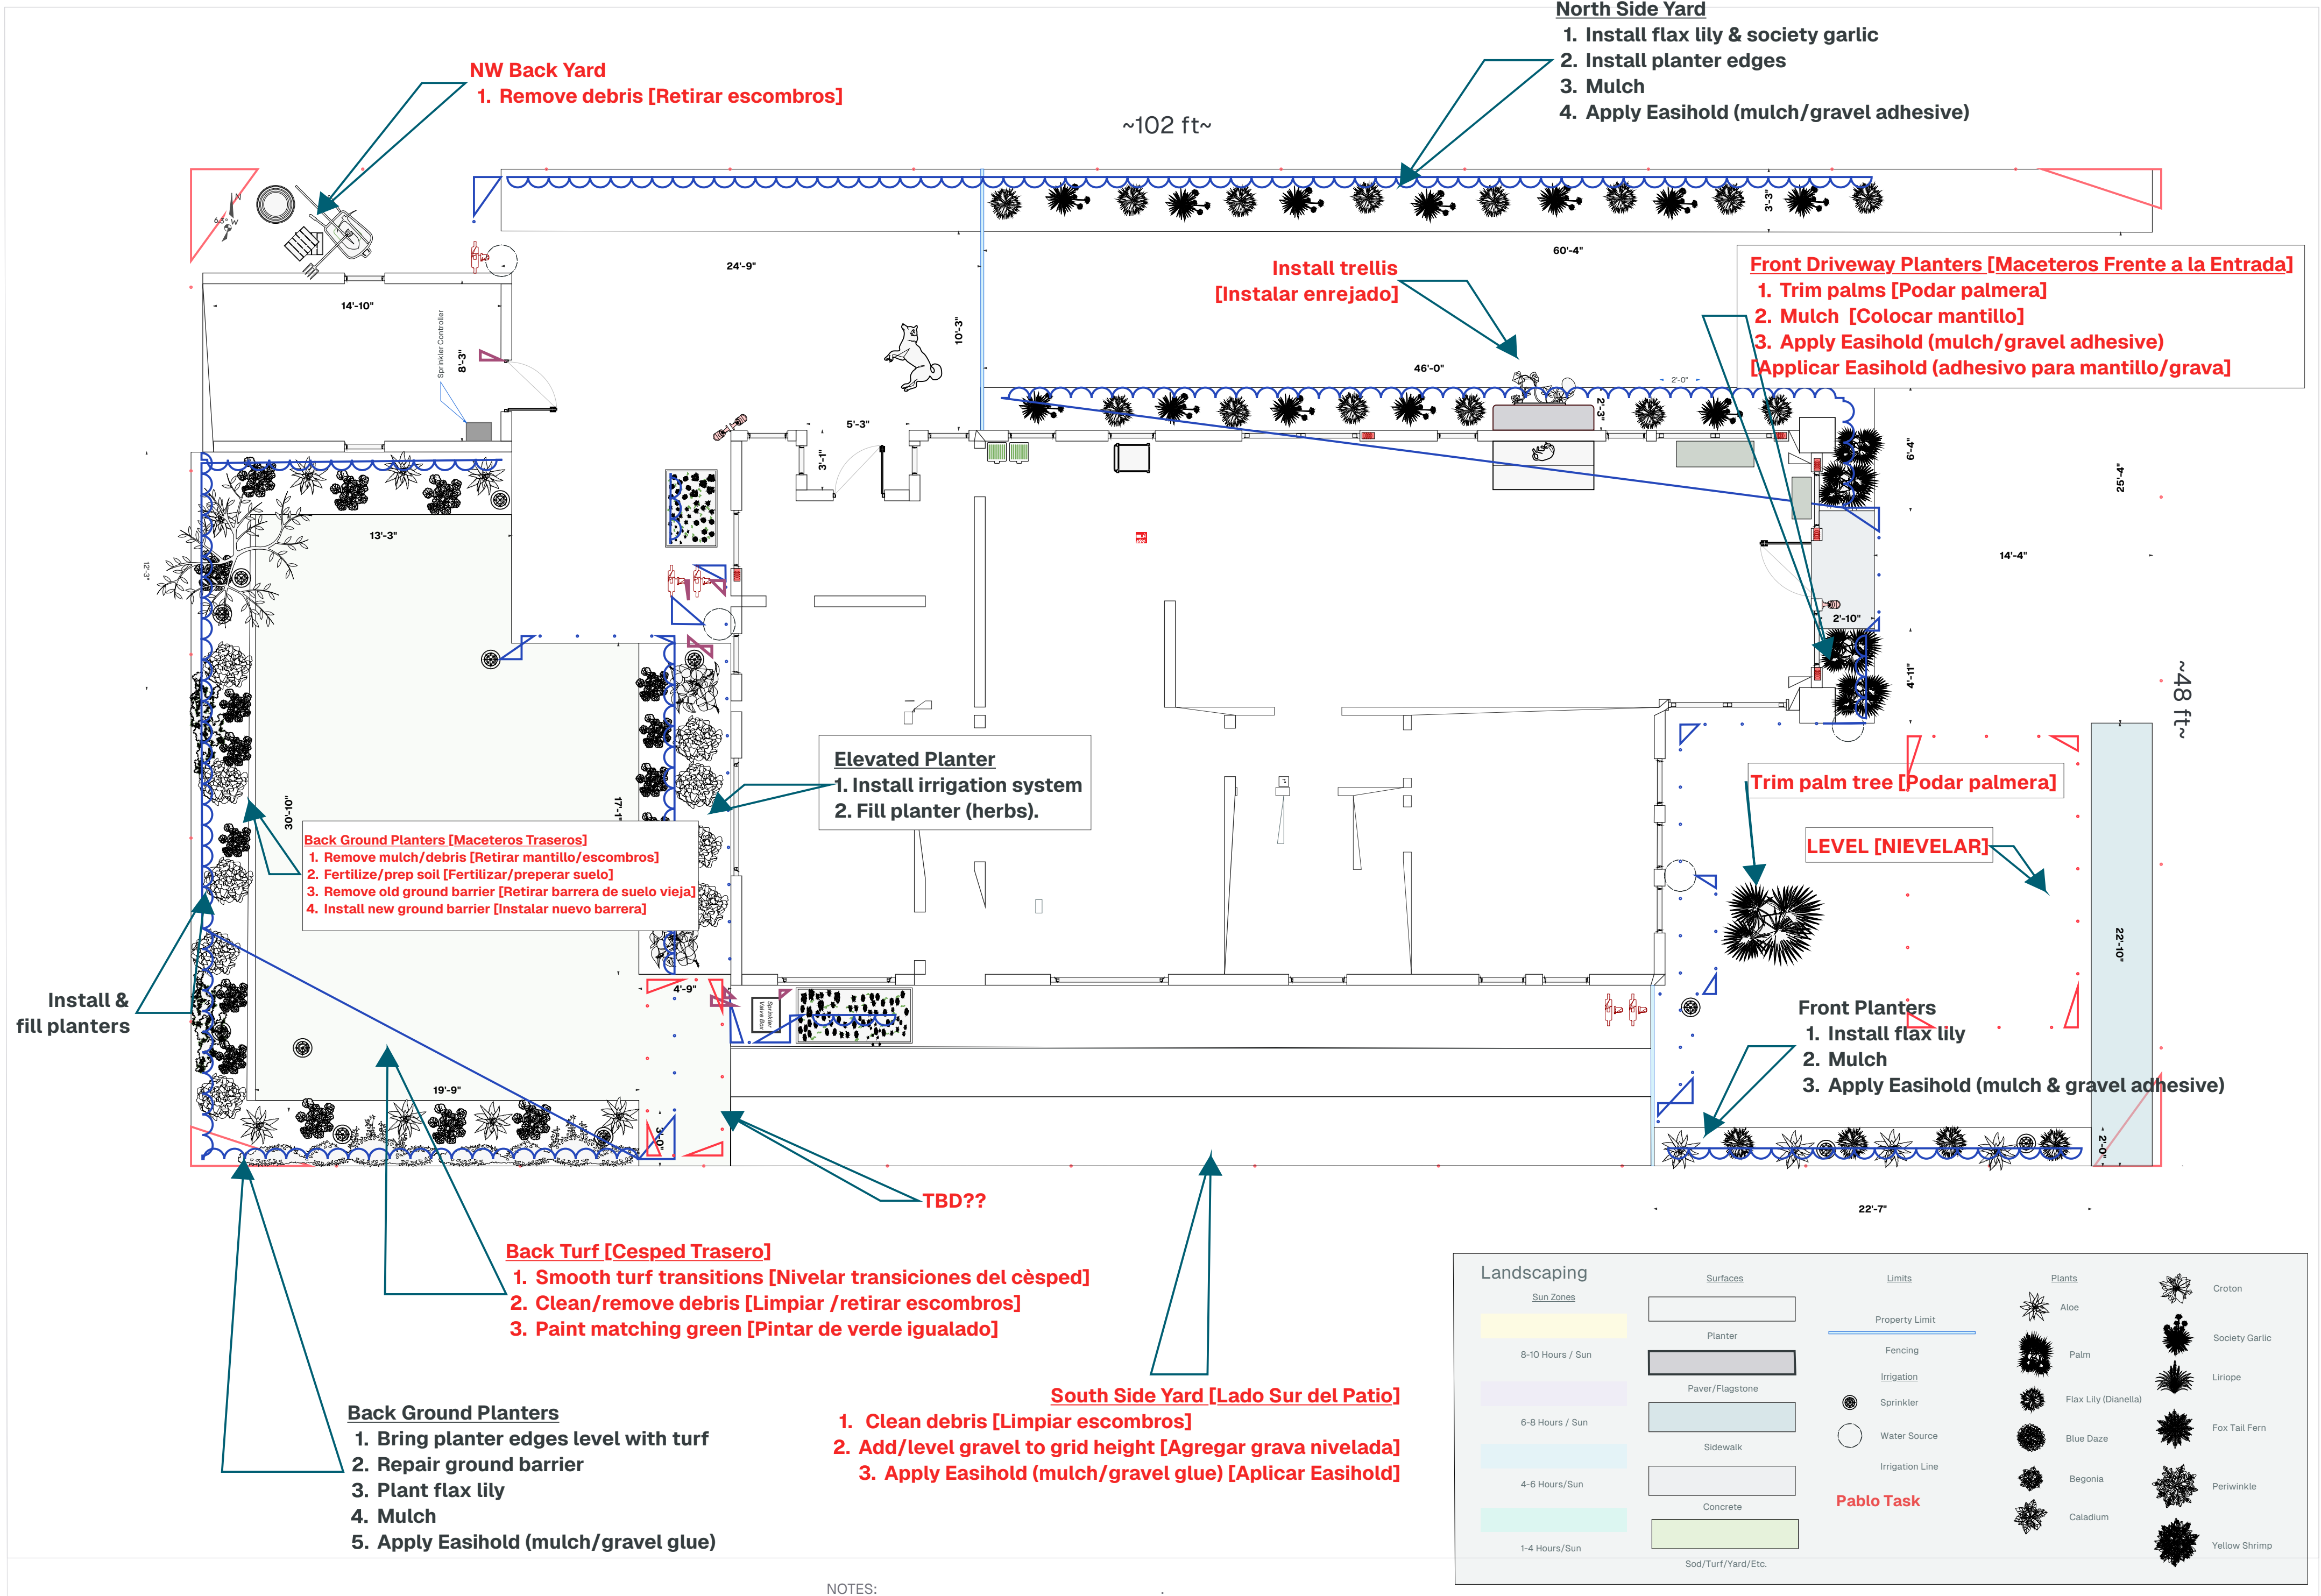

1.4


Lanscaping - Tasks December 2025


SCALE
1:3/16

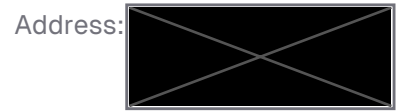

Made by : Justin Lenhart

Date : 24 Nov 2025

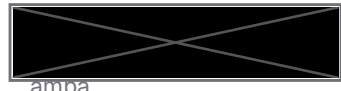

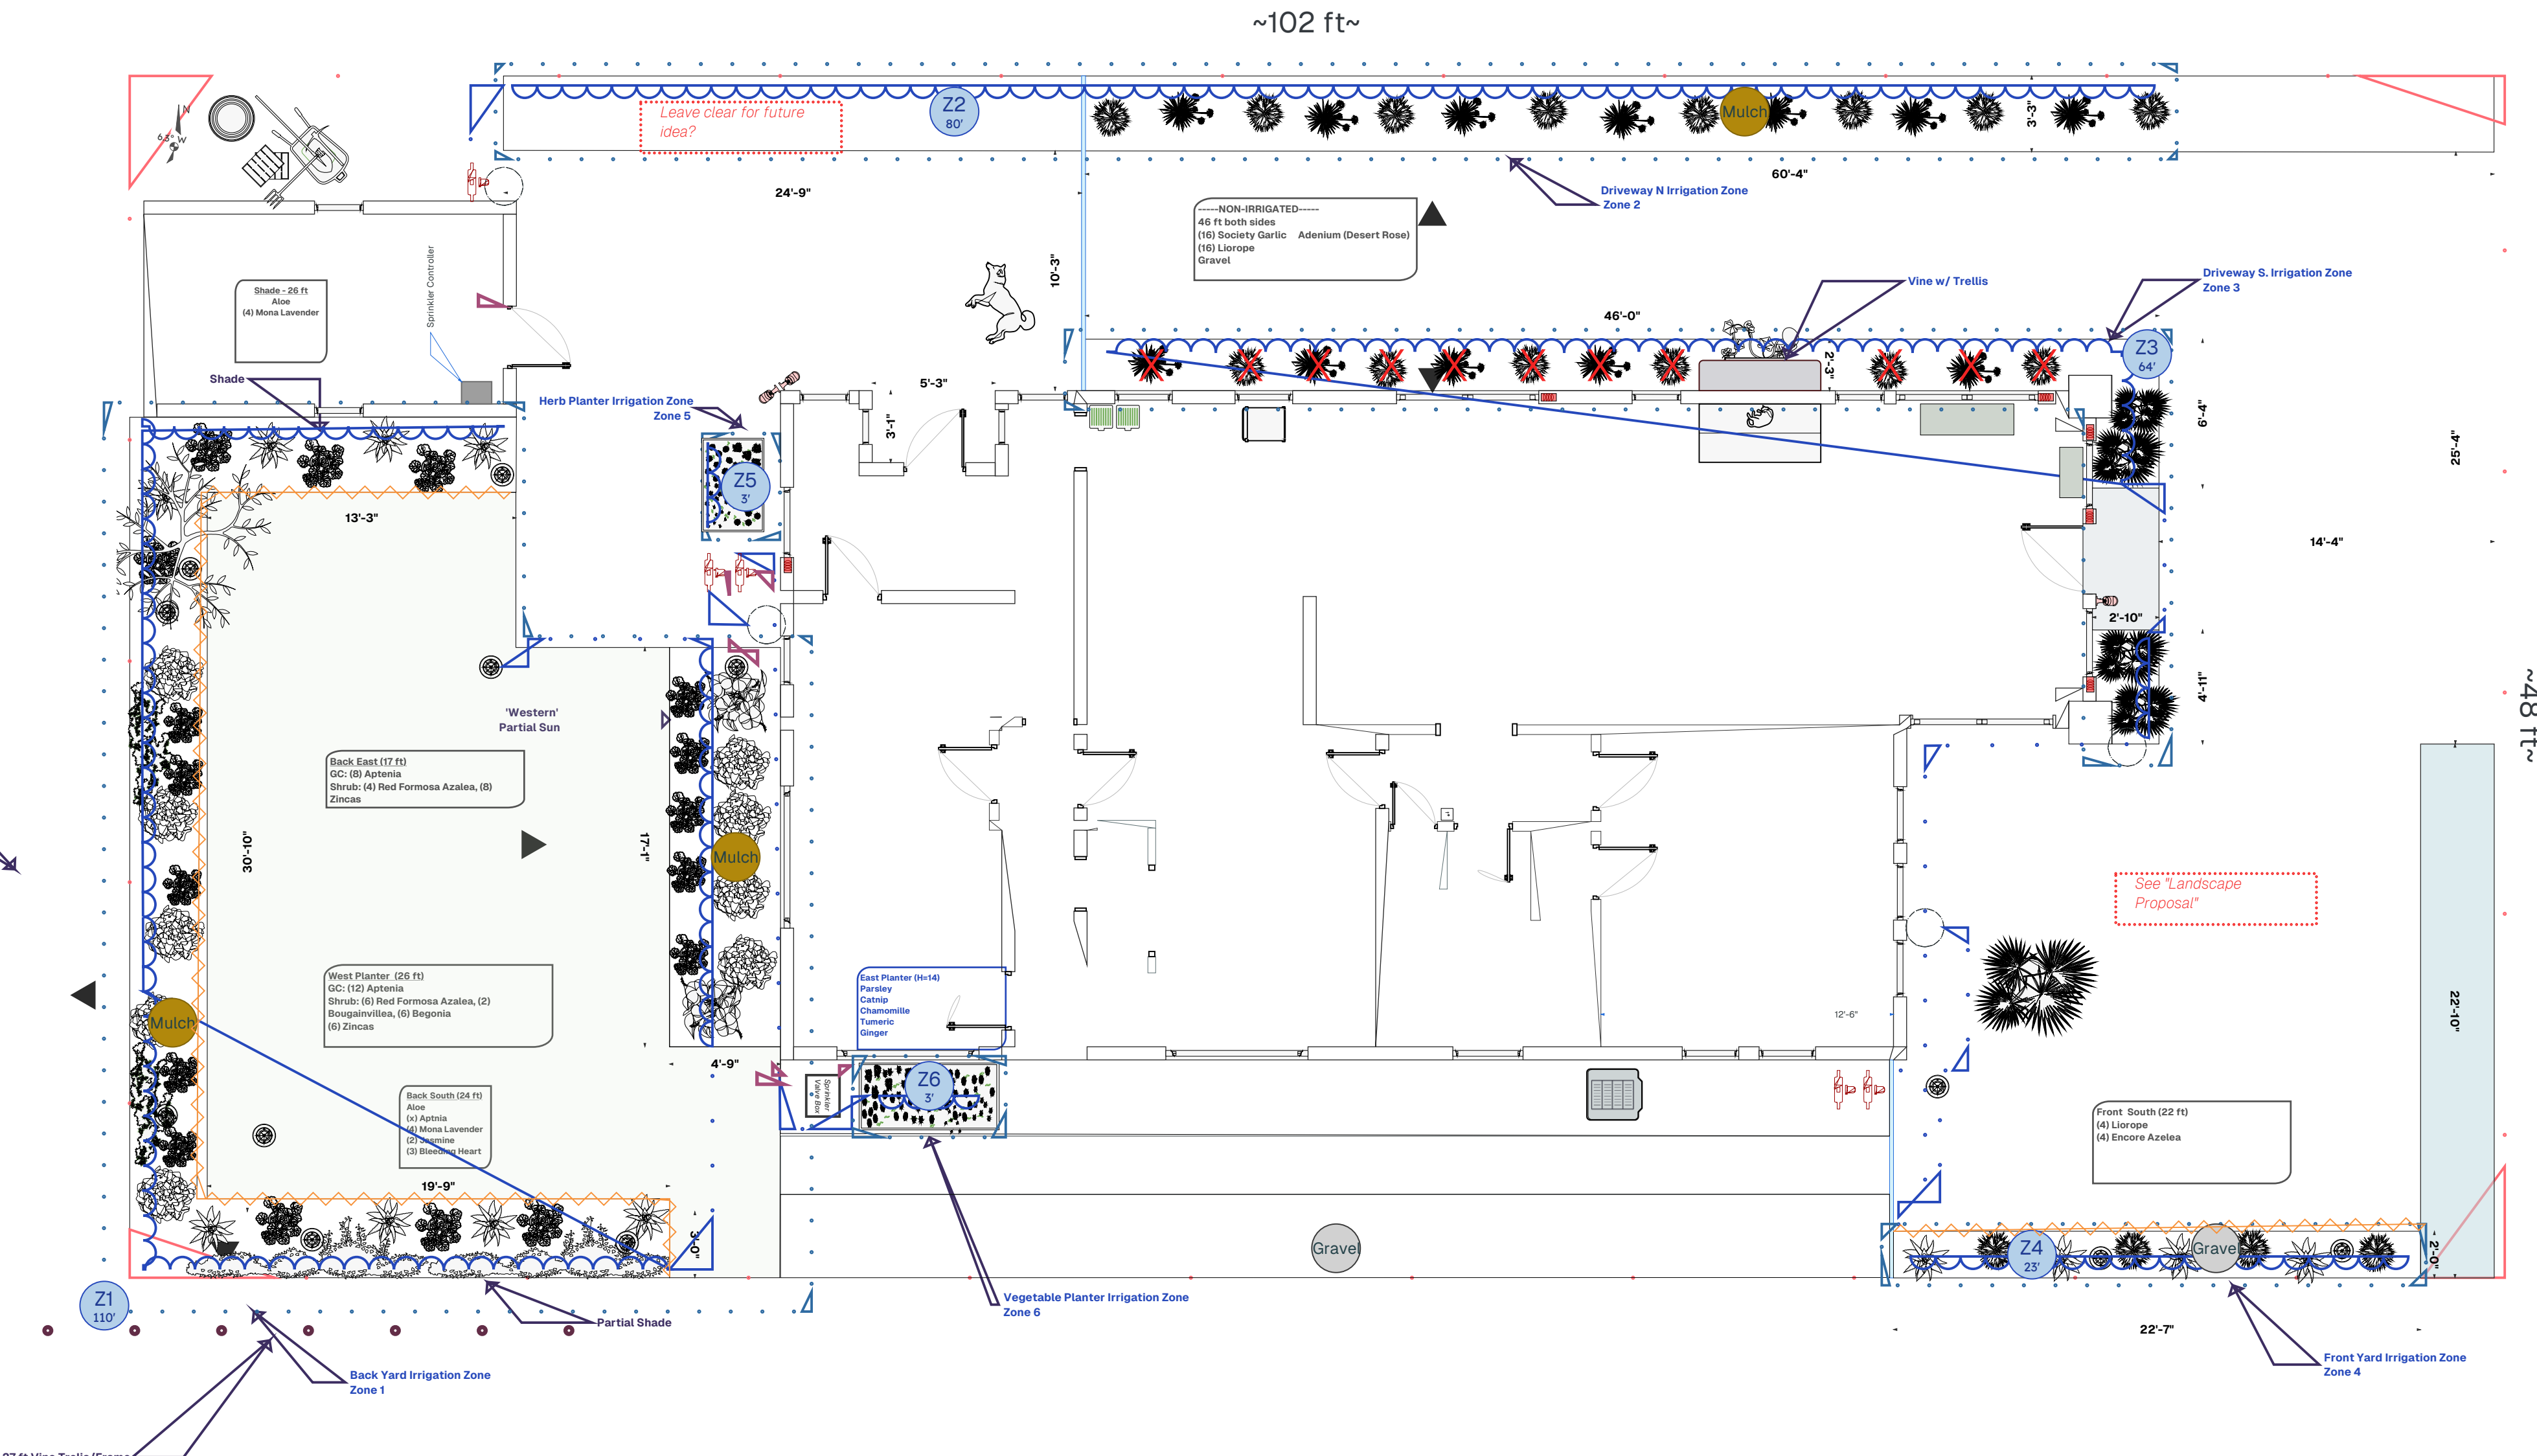

Landscaping

Sun Zones

8-10 Hours / Sun

6-8 Hours / Sun

4-6 Hours/Sun

1-4 Hours/Sun

Surfaces

Planter

Paver/Flagstone

Sidewalk

Concrete

Sod/Turf/Yard/Etc.

Limits

Property Limit

Fencing

Sprinkler

Water Source

Irrigation Line

Plants

Aloe

Palm

Flax Lily (Dianella)

Blue Daze

Begonia

Caladium

Croton

Society Garlic

Liriope

Fox Tail Fern

Periwinkle

Yellow Shrimp

A1.5

Landscaping/Irrigation - Plan

SCALE
1:3/16

NOTES:
1. Mulch & Gravel Required Assumptions
Mulch calculated at depth = 3 inches
Gravel calculated at depth = 2 inches
2. Plant Installation Notes

Address: [Redacted]

Made by : Justin Lenhart

Date : 24 Nov 2025

Tampa, FL

Project Bill of Materials

01


Item	Approval Code	Mfg./Product Name
Window, 3'-0"x3'0", SH	FL15906-R7	Andersen 100SHS3030

References

Florida-Friendly Landscaping Program..... <https://ffl.ifas.ufl.edu/resources/apps/plant-guide/>
South Florida Plant Guide.....<https://www.south-florida-plant-guide.com>
Florida Native Plant Society.....<https://www.fnps.org/#gsc.tab=0>

Desert Rose
Adenium obesum

Type.....Succulent / Caudex
Zone..... 10–11
Light.....Full sun
Soil..... Very well-drained; sandy/gritty
Height..... 1–3 ft
Spacing..... 2–3 ft
Water Sched. 1x/week (light); allow soil to fully dry between watering
Ideal pH..... 6.0–7.0
Soil Moist..... 10–20%

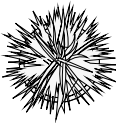

Bougainvillea
Bougainvillea spp.

Type.....Shrub / Vine
Zone..... 9–11
Light.....Full sun
Soil..... Well-drained; sandy preferred
Height..... 6–20 ft (climbing/spreading)
Spacing..... 4–10 ft
Water Sched. 1x/week (deep); very drought tolerant once established
Ideal pH..... 5.5–6.5
Soil Moist..... 15–25%




Formosa Azalea
Rhododendron indicum (Formosa)

Type.....Shrub
Zone..... 8–10
Light.....Partial sun to partial shade
Soil..... Well-drained; acidic
Height..... 6–10 ft
Spacing..... 4–6 ft
Water Sched. 2–3x/week (establish), then 1x/week; increase in heat
Ideal pH..... 4.5–6.0
Soil Moist..... Medium (keep consistently moist, not soggy)




Aptenia
Aptenia cordifolia

Type.....Groundcover (succulent)
Zone..... 9–11
Light.....Full sun to partial sun
Soil..... Well-drained; sandy
Height..... 0.5–1 ft
Spacing..... 1–2 ft
Water Sched. 1x/week; drought tolerant once established
Ideal pH..... 6.0–7.5
Soil Moist..... 20–30%

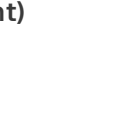

Begonia
Begonia spp.

Type.....Perennial / Annual
Zone..... 9–11
Light.....Partial shade to full shade
Soil..... Moist, well-drained; organic-rich
Height..... 0.5–1.5 ft
Spacing..... 1–1.5 ft
Water Sched. 2–3x/week (light); keep evenly moist, not soggy
Ideal pH..... 5.5–6.5
Soil Moist..... 40–55%

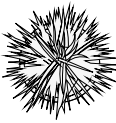

'Encore' Azalea
Rhododendron hybrid

Type.....Shrub
Zone..... 6–10
Light.....Partial sun to full sun
Soil..... Well-drained; acidic
Height..... 3–5 ft
Spacing..... 3–4 ft
Water Sched. 2x/week first year, then every 7–10 days; more in heat
Ideal pH..... 4.5–6.0
Soil Moist..... Medium




Zinnia ('Zinca')
Zinnia elegans

Type.....Annual
Zone..... 3–11
Light.....Full sun
Soil..... Well-drained
Height..... 1–3 ft
Spacing..... 1–2 ft
Water Sched. 2–3x/week (light watering); avoid soggy soil
Ideal pH..... 5.5–7.5
Soil Moist..... 25–35%



Liriope
Liriope muscari

Type.....Groundcover
Zone..... 8–11
Light.....Full sun to partial shade
Soil..... Well-drained
Height..... 1–1.5 ft
Spacing..... 1–2 ft
Water Sched. 1x/week; very drought tolerant once established
Ideal pH..... 6.0–7.5
Soil Moist..... 20–30%

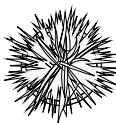


Flax Lily
dianella tasmanica

Type.....Perennial
Zone..... 8a–11
Light.....Partial to full sun
Soil..... Well-drained; acid to slightly alkaline (5.4–7.2)
Height..... 2 ft H
Spacing..... 2–2.5 ft
Water Sched.
Ideal pH.....
Soil Moist.....




Mona Lavender
Plectranthus 'Mona Lavender'

Type.....Perennial
Zone..... 9–11
Light.....Partial shade
Soil..... Well-drained; organic
Height..... 1–2 ft
Spacing..... 1–2 ft
Water Sched. 2x/week; keep consistent moisture
Ideal pH..... 5.5–7.5
Soil Moist..... 35–45%

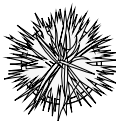

Bleeding Heart Wine
Clerodendrum thomsoniae

Type.....Vine
Zone..... 9–11
Light.....Partial sun to partial shade
Soil..... Well-drained; organic-rich
Height..... 10–15 ft
Spacing..... 3–6 ft
Water Sched. 2–3x/week; keep consistently moist but not soggy
Ideal pH..... 6.0–7.0
Soil Moist..... 40–55%

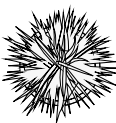


Society Garlic
Tulbaghia violacea

Type.....Perennial
Zone..... 8–11
Light.....Full sun
Soil..... Well-drained
Height..... 1–2 ft
Spacing..... 1–2 ft
Water Sched. 1x/week; drought tolerant once established
Ideal pH..... 6.0–7.5
Soil Moist..... 20–30%



Jasmine
Jasminum spp.

Type.....Shrub / vine
Zone..... 8–11
Light.....Full sun to partial shade
Soil..... Well-drained
Height..... 3–10 ft
Spacing..... 3–6 ft
Water Sched. 1–2x/week; more during bloom/heat
Ideal pH..... 6.0–7.5
Soil Moist..... 30–40%

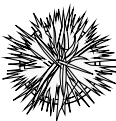

A7.1

Reference

SCALE
1:1/4

NOTES:

1. Scope of work:

- replacement of all existing windows with like-for-like American Craftsman 70 Series Single Hung units.
- No change to rough openings, structural framework, headers, sills, or walls.
- All installation performed per manufacturer instructions and Florida Product Approval FL 14911 (Rev. 12).
- All replacement windows match or exceed existing sizes.

2. Installation requirements

- Fasteners, anchor spacing, shims, and sealants installed per installation instructions in FL14911 approval file.
- All windows HVHZ rated, impact-rated, tested to TAS 201/202/203.
- Sill pan flashing, jamb flashing, and head flashing per ASTM E2112 and FBC R703.4.

3. Energy & safety:

- Windows meet FBC R402.3 and labeled with NFRC sticker; code compliant glazing per FBC R308 (no tempered glass required).


4. Bedroom windows:

- All existing windows retain or exceed original clear opening.

5. Homeowner Builder:

- Permit pulled under Homeowner/Builder exemption. **All installation work performed by properly licensed contractor.**

Address:

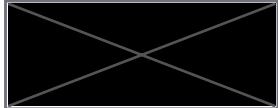

Made by : Justin Lenhart

Date : 24 Nov 2025



4"

14'-4"

4'-11"

2'-10"

Landscape fabric (ID 04) to go under deck area only-

13'-4"

(2) fasteners per deck/joist intersection

Deck planking pulled away for detail beneath

Center support pedestal every other joist

Cross-joist offset for pedestal clearance

Pedestal base tangent to skirt

12'-1 1/2"

3. Other Information:

• Windows meet FBC R402.3 and labeled with NFRC sticker; code compliant glazing per FBC R308 (no tempered glass required).

Address:

Made by : Justin Lenhart

Date : 24 Nov 2025

NOTES: 1. Scope of work:

2. Notes

Front Yard Detail

SCALE
1:1/4



A1.6



Tampa, FL